



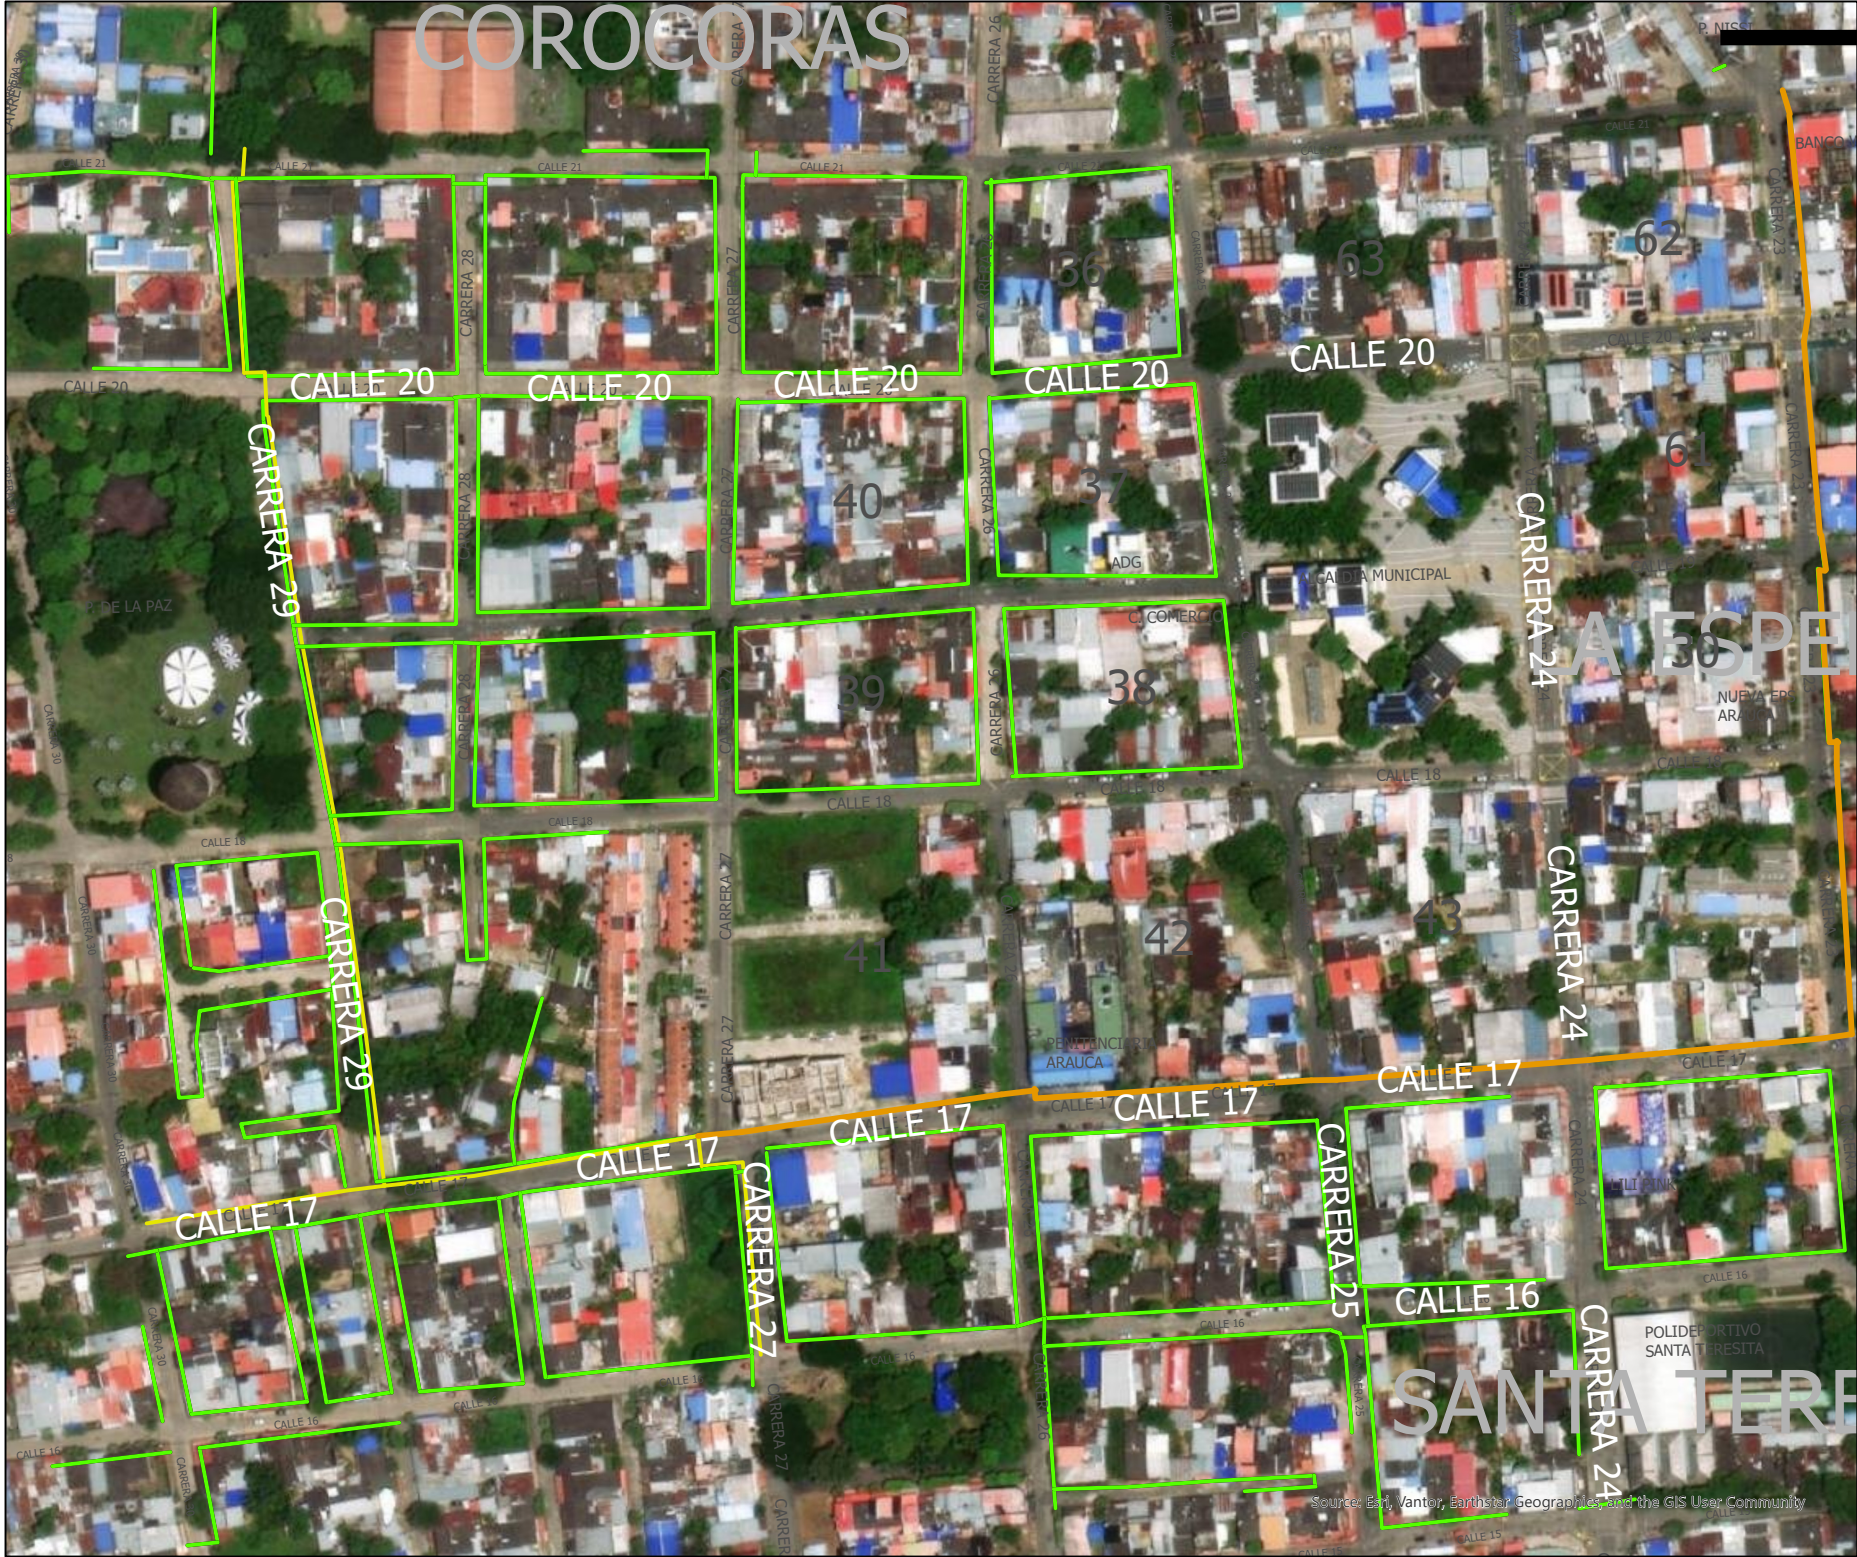

DISEÑO DE REDES DE DISTRIBUCIÓN
DE GAS DOMICILIARIO
EN EL MUNICIPIO DE ARAUCA
(TRONCALES Y ANILLOS)

LEYENDA	
TUBERÍAS	ESTACION GLP
 TUBERÍA 3/4"	 ESTACION GLP
 TUBERÍA 3"	
 TUBERÍA 4"	
 TUBERÍA 6"	

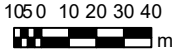

TUBERÍAS	LONGITUDES
 TUBERÍA 3/4"	109344 m
 TUBERÍA 3"	1025 m
 TUBERÍA 4"	2003 m
 TUBERÍA 6"	514 m

ESCALA
1:13.000

PLANCHA
1/1

FECHA
SEP./2026