


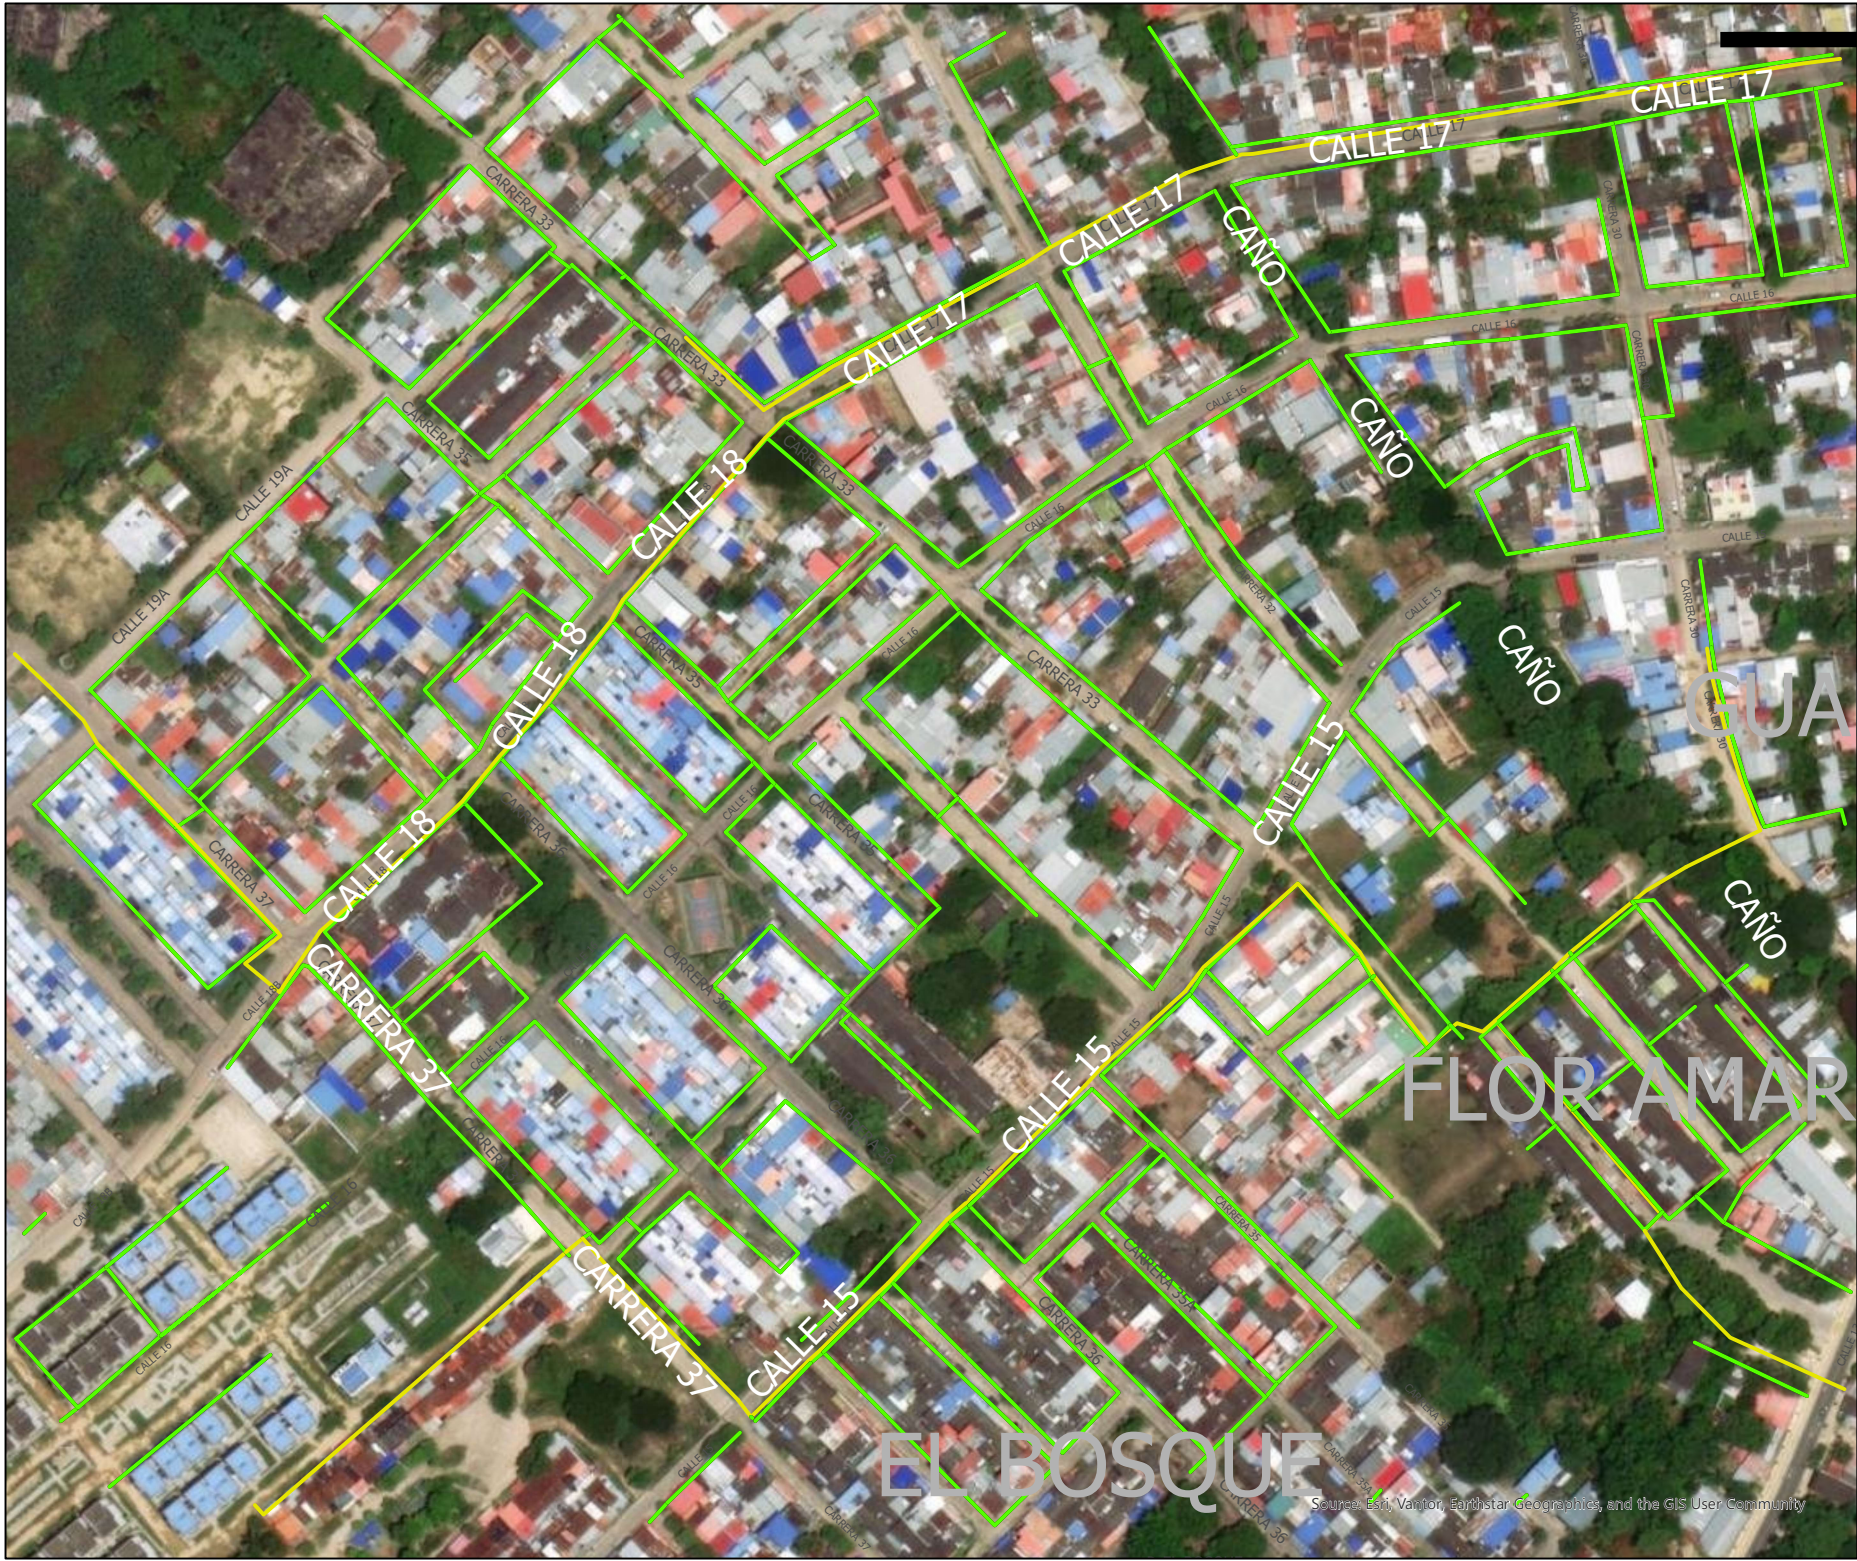

DISEÑO DE REDES DE DISTRIBUCIÓN
DE GAS DOMICILIARIO
EN EL MUNICIPIO DE ARAUCA
(TRONCALES Y ANILLOS)

LEYENDA

TUBERÍAS

ESTACION GLP

- TUBERÍA 3/4"
- TUBERÍA 3"
- TUBERÍA 4"
- TUBERÍA 6"

ESTACION
GLP

105 0 10 20 30 40

m

TUBERÍAS

LONGITUDES

- TUBERÍA 3/4"
- TUBERÍA 3"
- TUBERÍA 4"
- TUBERÍA 6"

109344 m
1025 m
2003 m
514 m

ESCALA

1:13.000

PLANCHA

1/1

FECHA

SEP./2026