


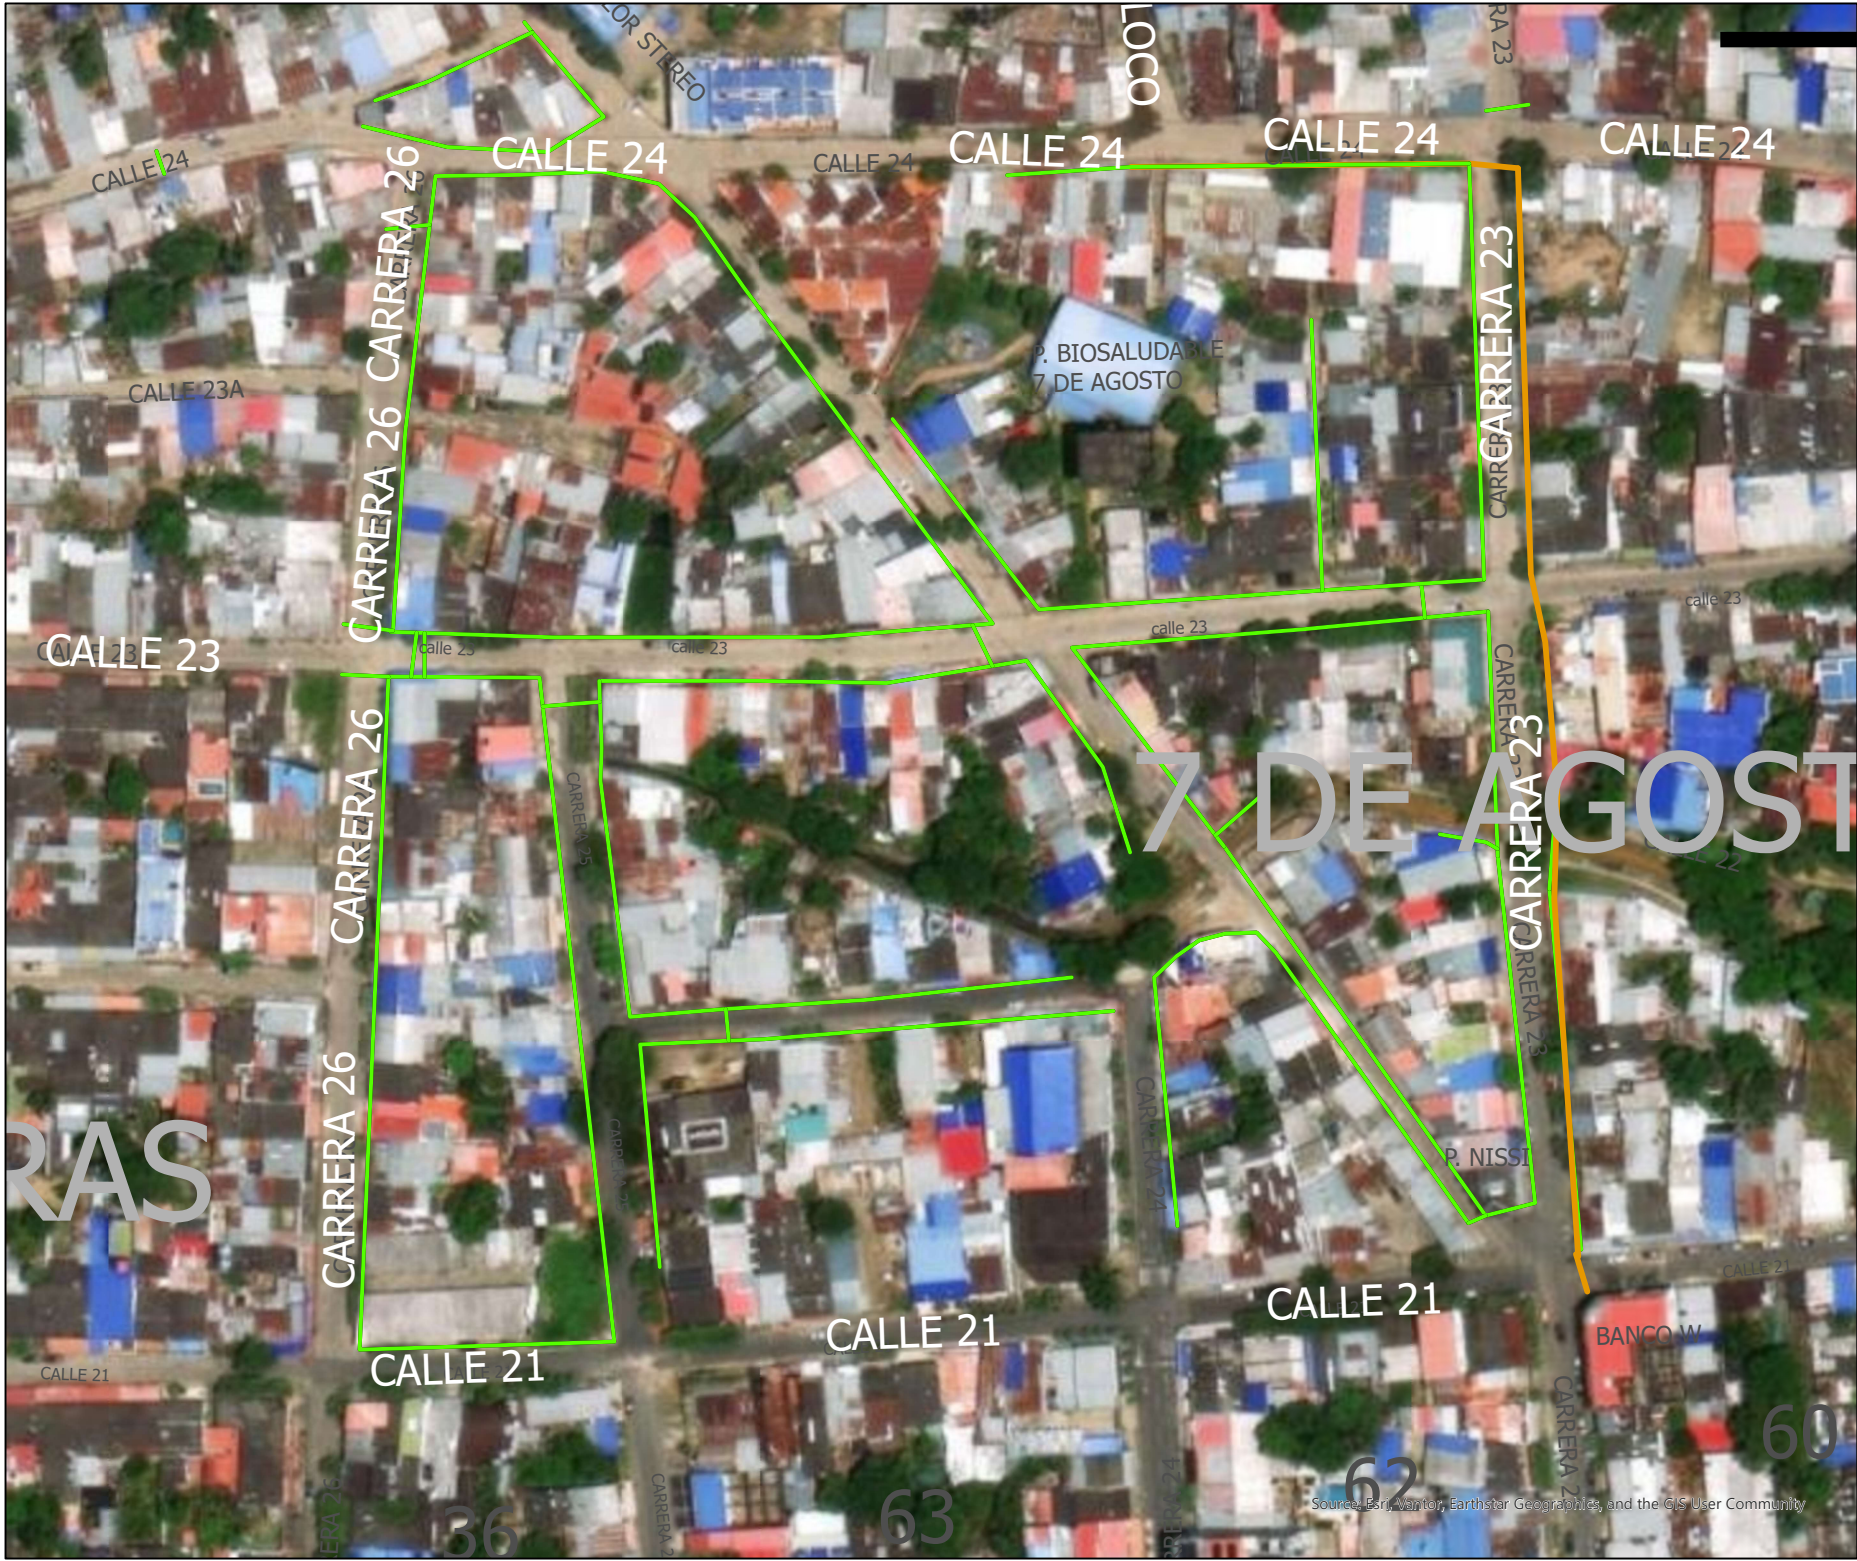

DISEÑO DE REDES DE DISTRIBUCIÓN
DE GAS DOMICILIARIO
EN EL MUNICIPIO DE ARAUCA
(TRONCALES Y ANILLOS)


LEYENDA

TUBERÍAS

ESTACION GLP

- TUBERÍA 3/4"
- TUBERÍA 3"
- TUBERÍA 4"
- TUBERÍA 6"

ESTACION GLP

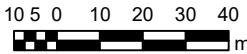

TUBERÍAS

LONGITUDES

- TUBERÍA 3/4" 109344 m
- TUBERÍA 3" 1025 m
- TUBERÍA 4" 2003 m
- TUBERÍA 6" 514 m

ESCALA

1:13.000

PLANCHA

1/1

FECHA

SEP./2026